


Independent residence · Balanced concept (Option A) · v08 · 28 Sep 2026



Concept drawing — not for construction.
Clear room sizes inside finished walls.
Walls: 9" external, 4.5" internal. Plan cut at 4 ft.

FIRST FLOOR PLAN (2nd floor, future: same) | FFL +13'-0" | floor-to-floor 10'-0"



Independent residence · Balanced concept (Option A) · v08 · 28 Sep 2026

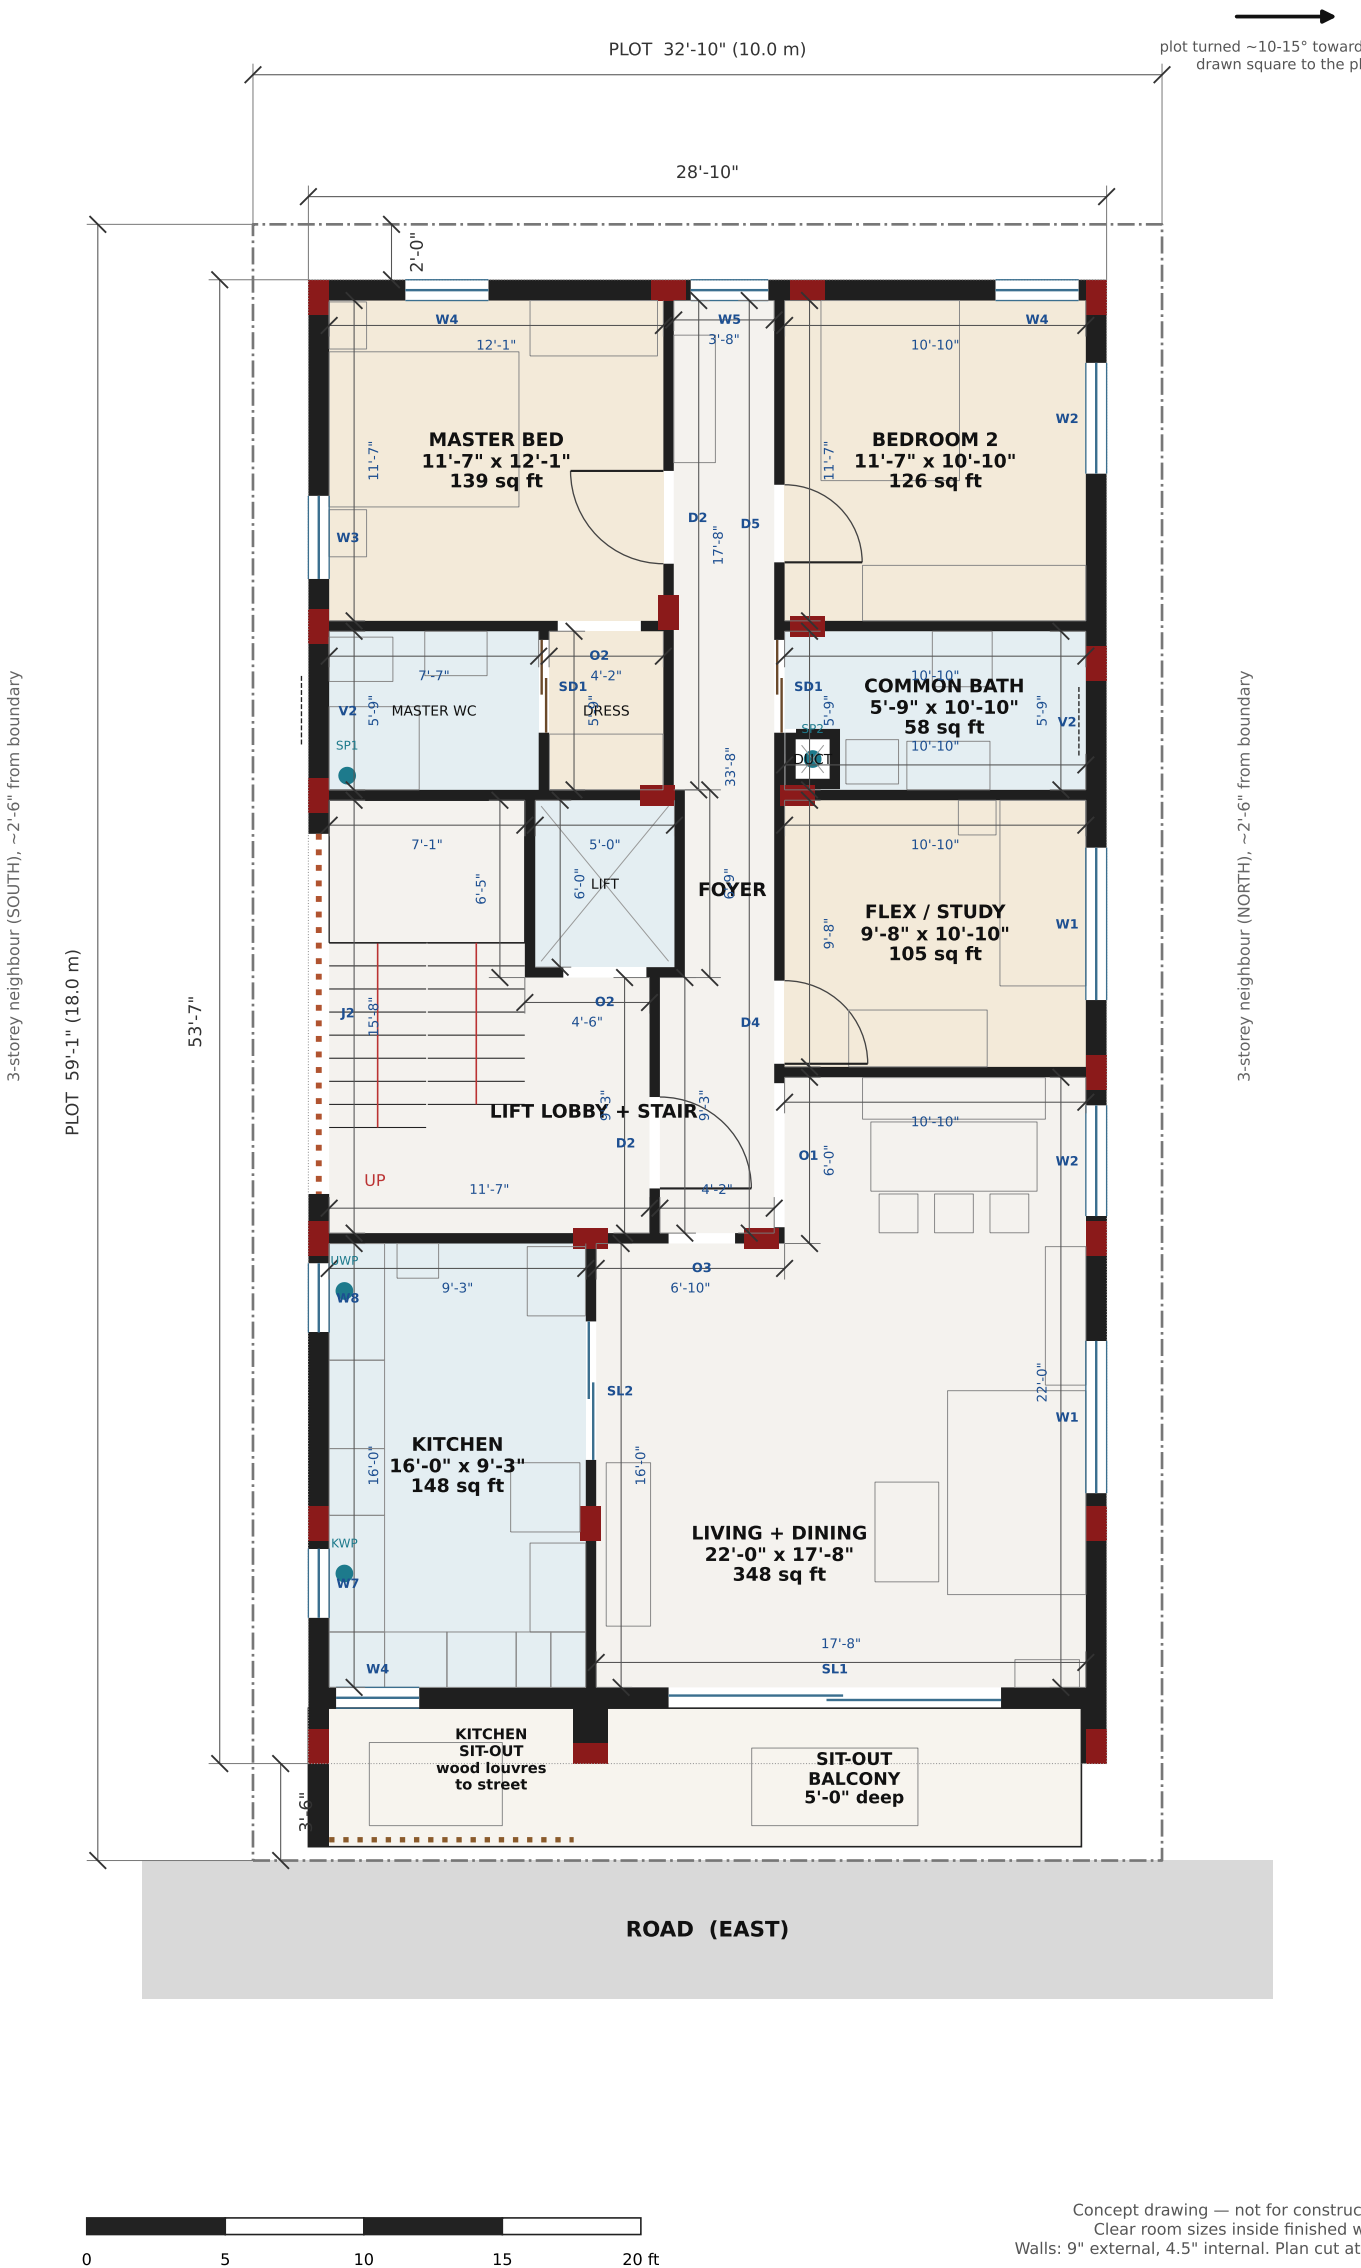

TERRACE PLAN | Roof +23'-0" | parapet 3'-0"

Independent residence · Balanced concept (Option A) · v08 · 28 Sep 2026



→ N
plot turned ~10-15° toward south;
drawn square to the plot

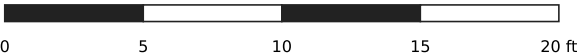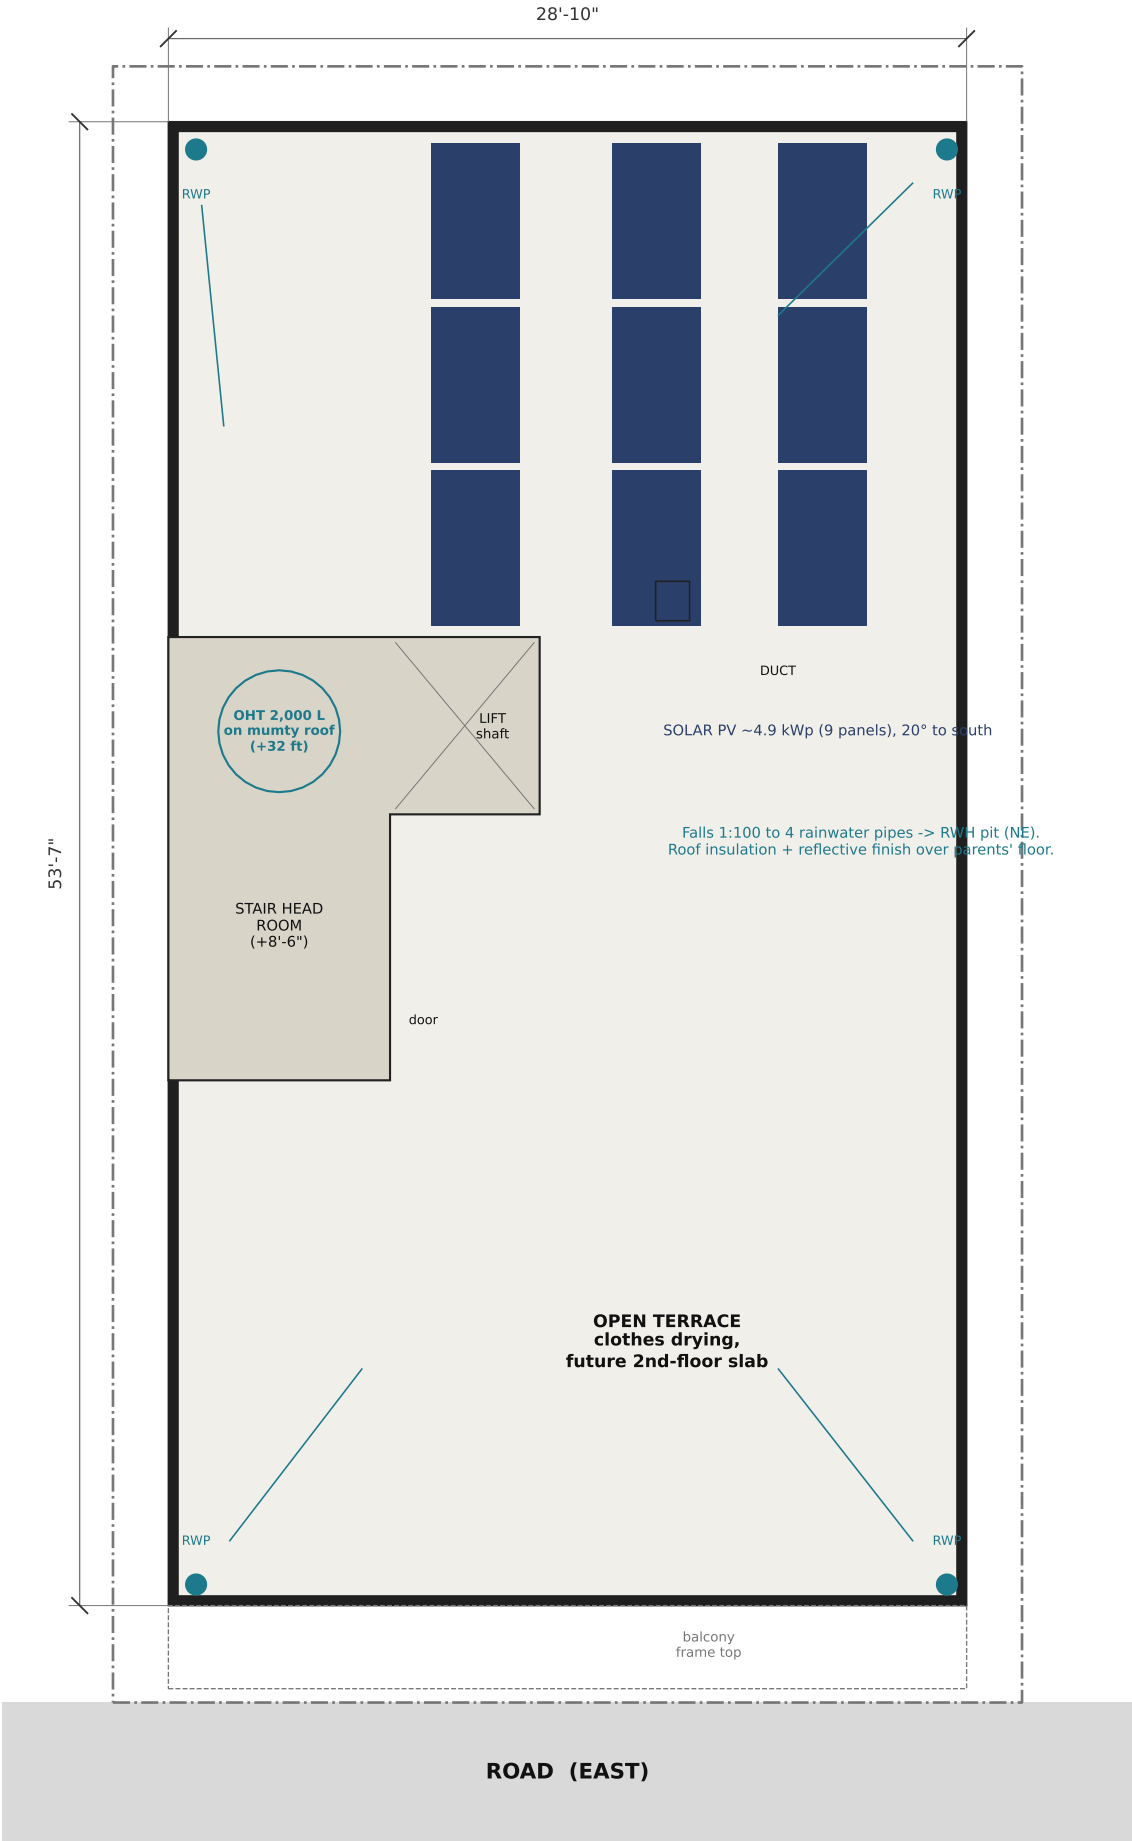

Concept drawing — not for construction.
Clear room sizes inside finished walls.
Walls: 9" external, 4.5" internal. Plan cut at 4 ft.

COLUMN LAYOUT (preliminary, for the structural engineer) | RCC frame designed for G+2; Phase 1 builds G+1

Independent residence · Balanced concept (Option A) · v08 · 28 Sep 2026

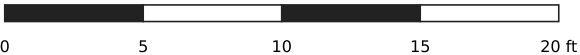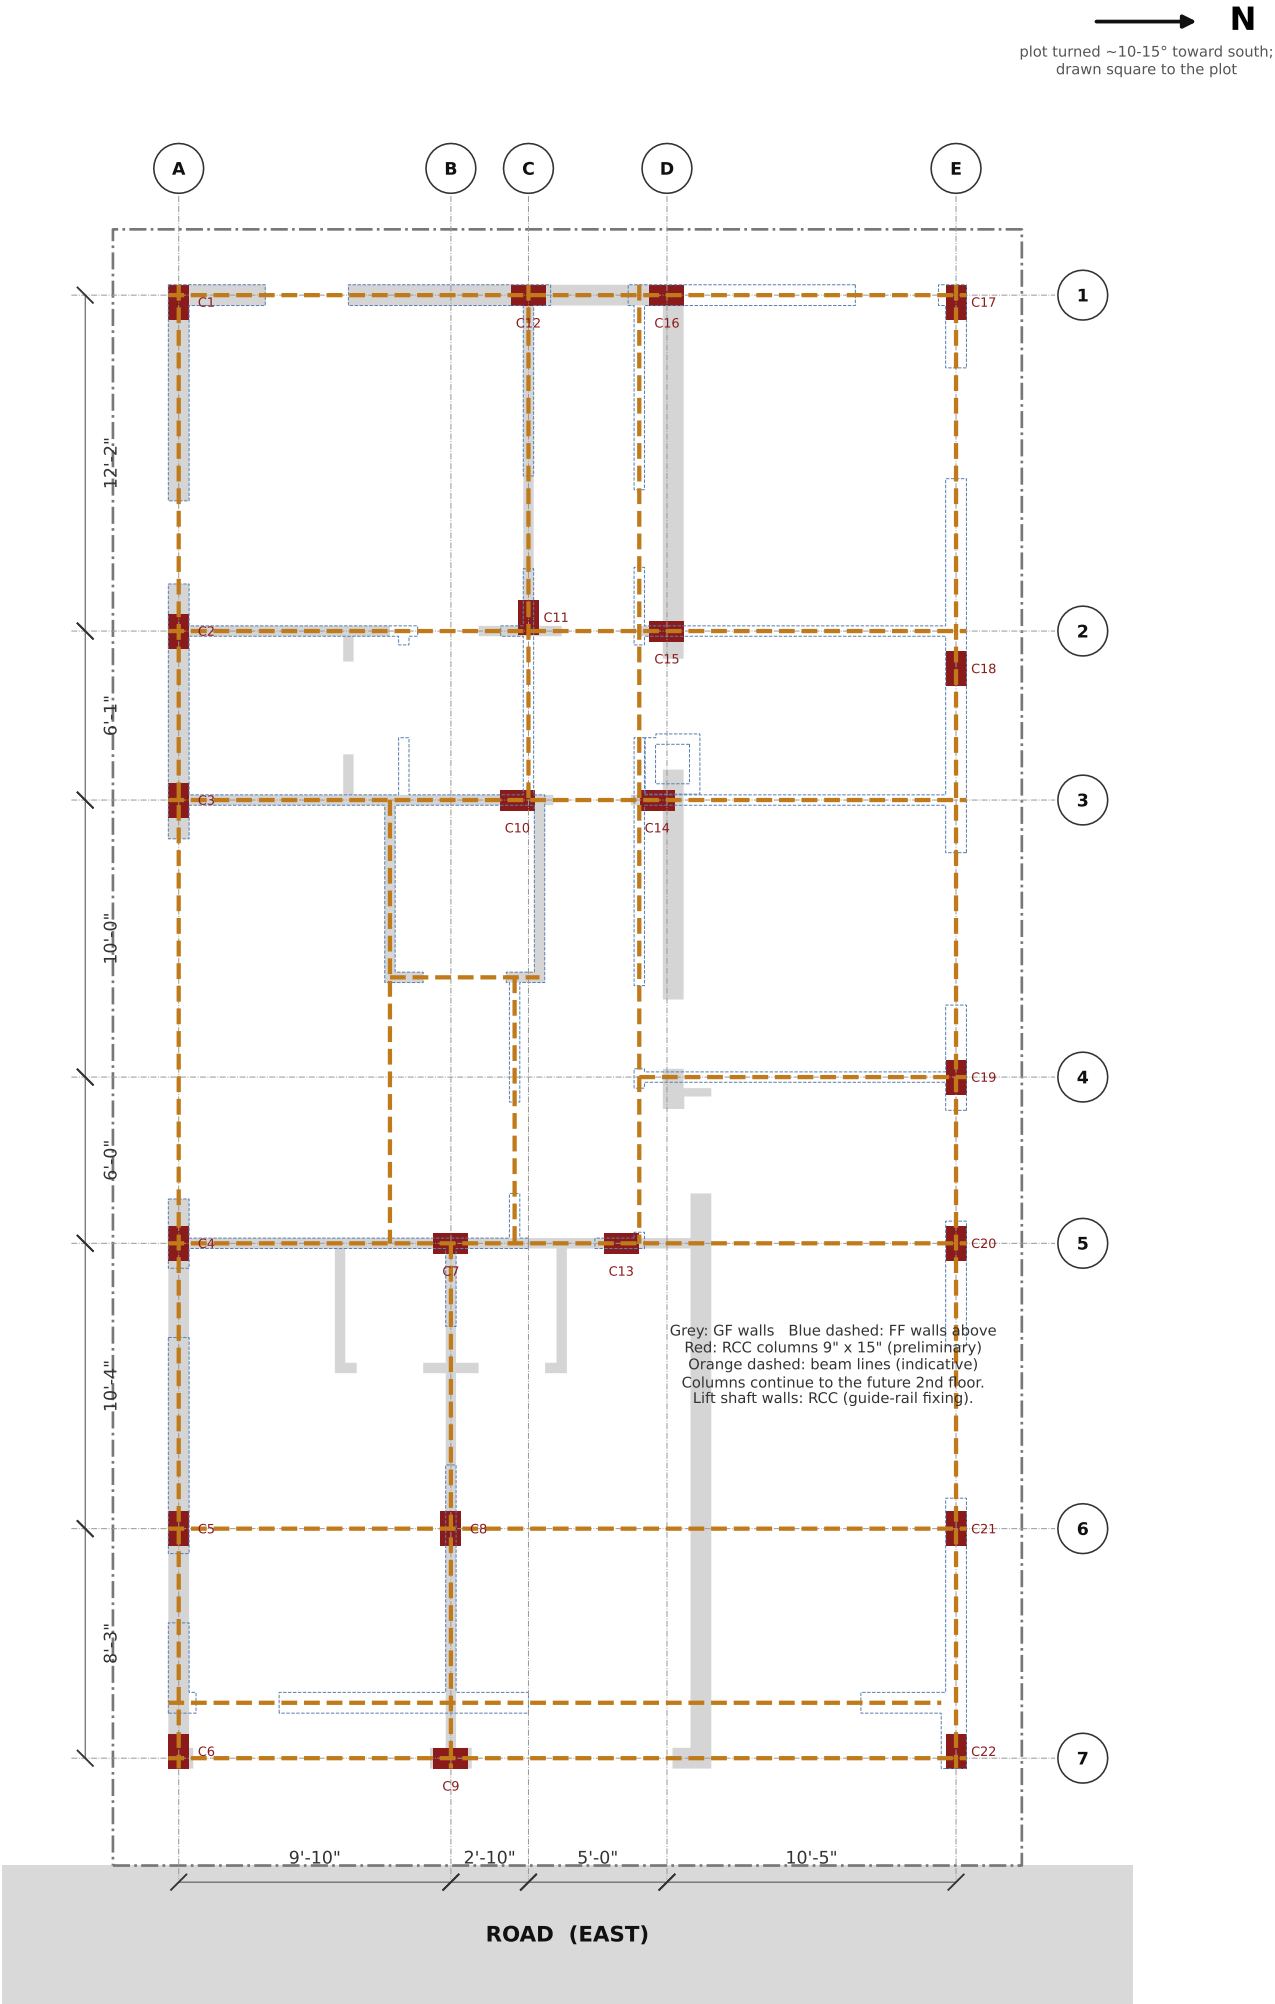

Concept drawing — not for construction.
Clear room sizes inside finished walls.
Walls: 9" external, 4.5" internal. Plan cut at 4 ft.